INSTALACIÓN SISTEMA DE FRIO - CALOR

A DISTRIBUCIÓN EDIFICIO

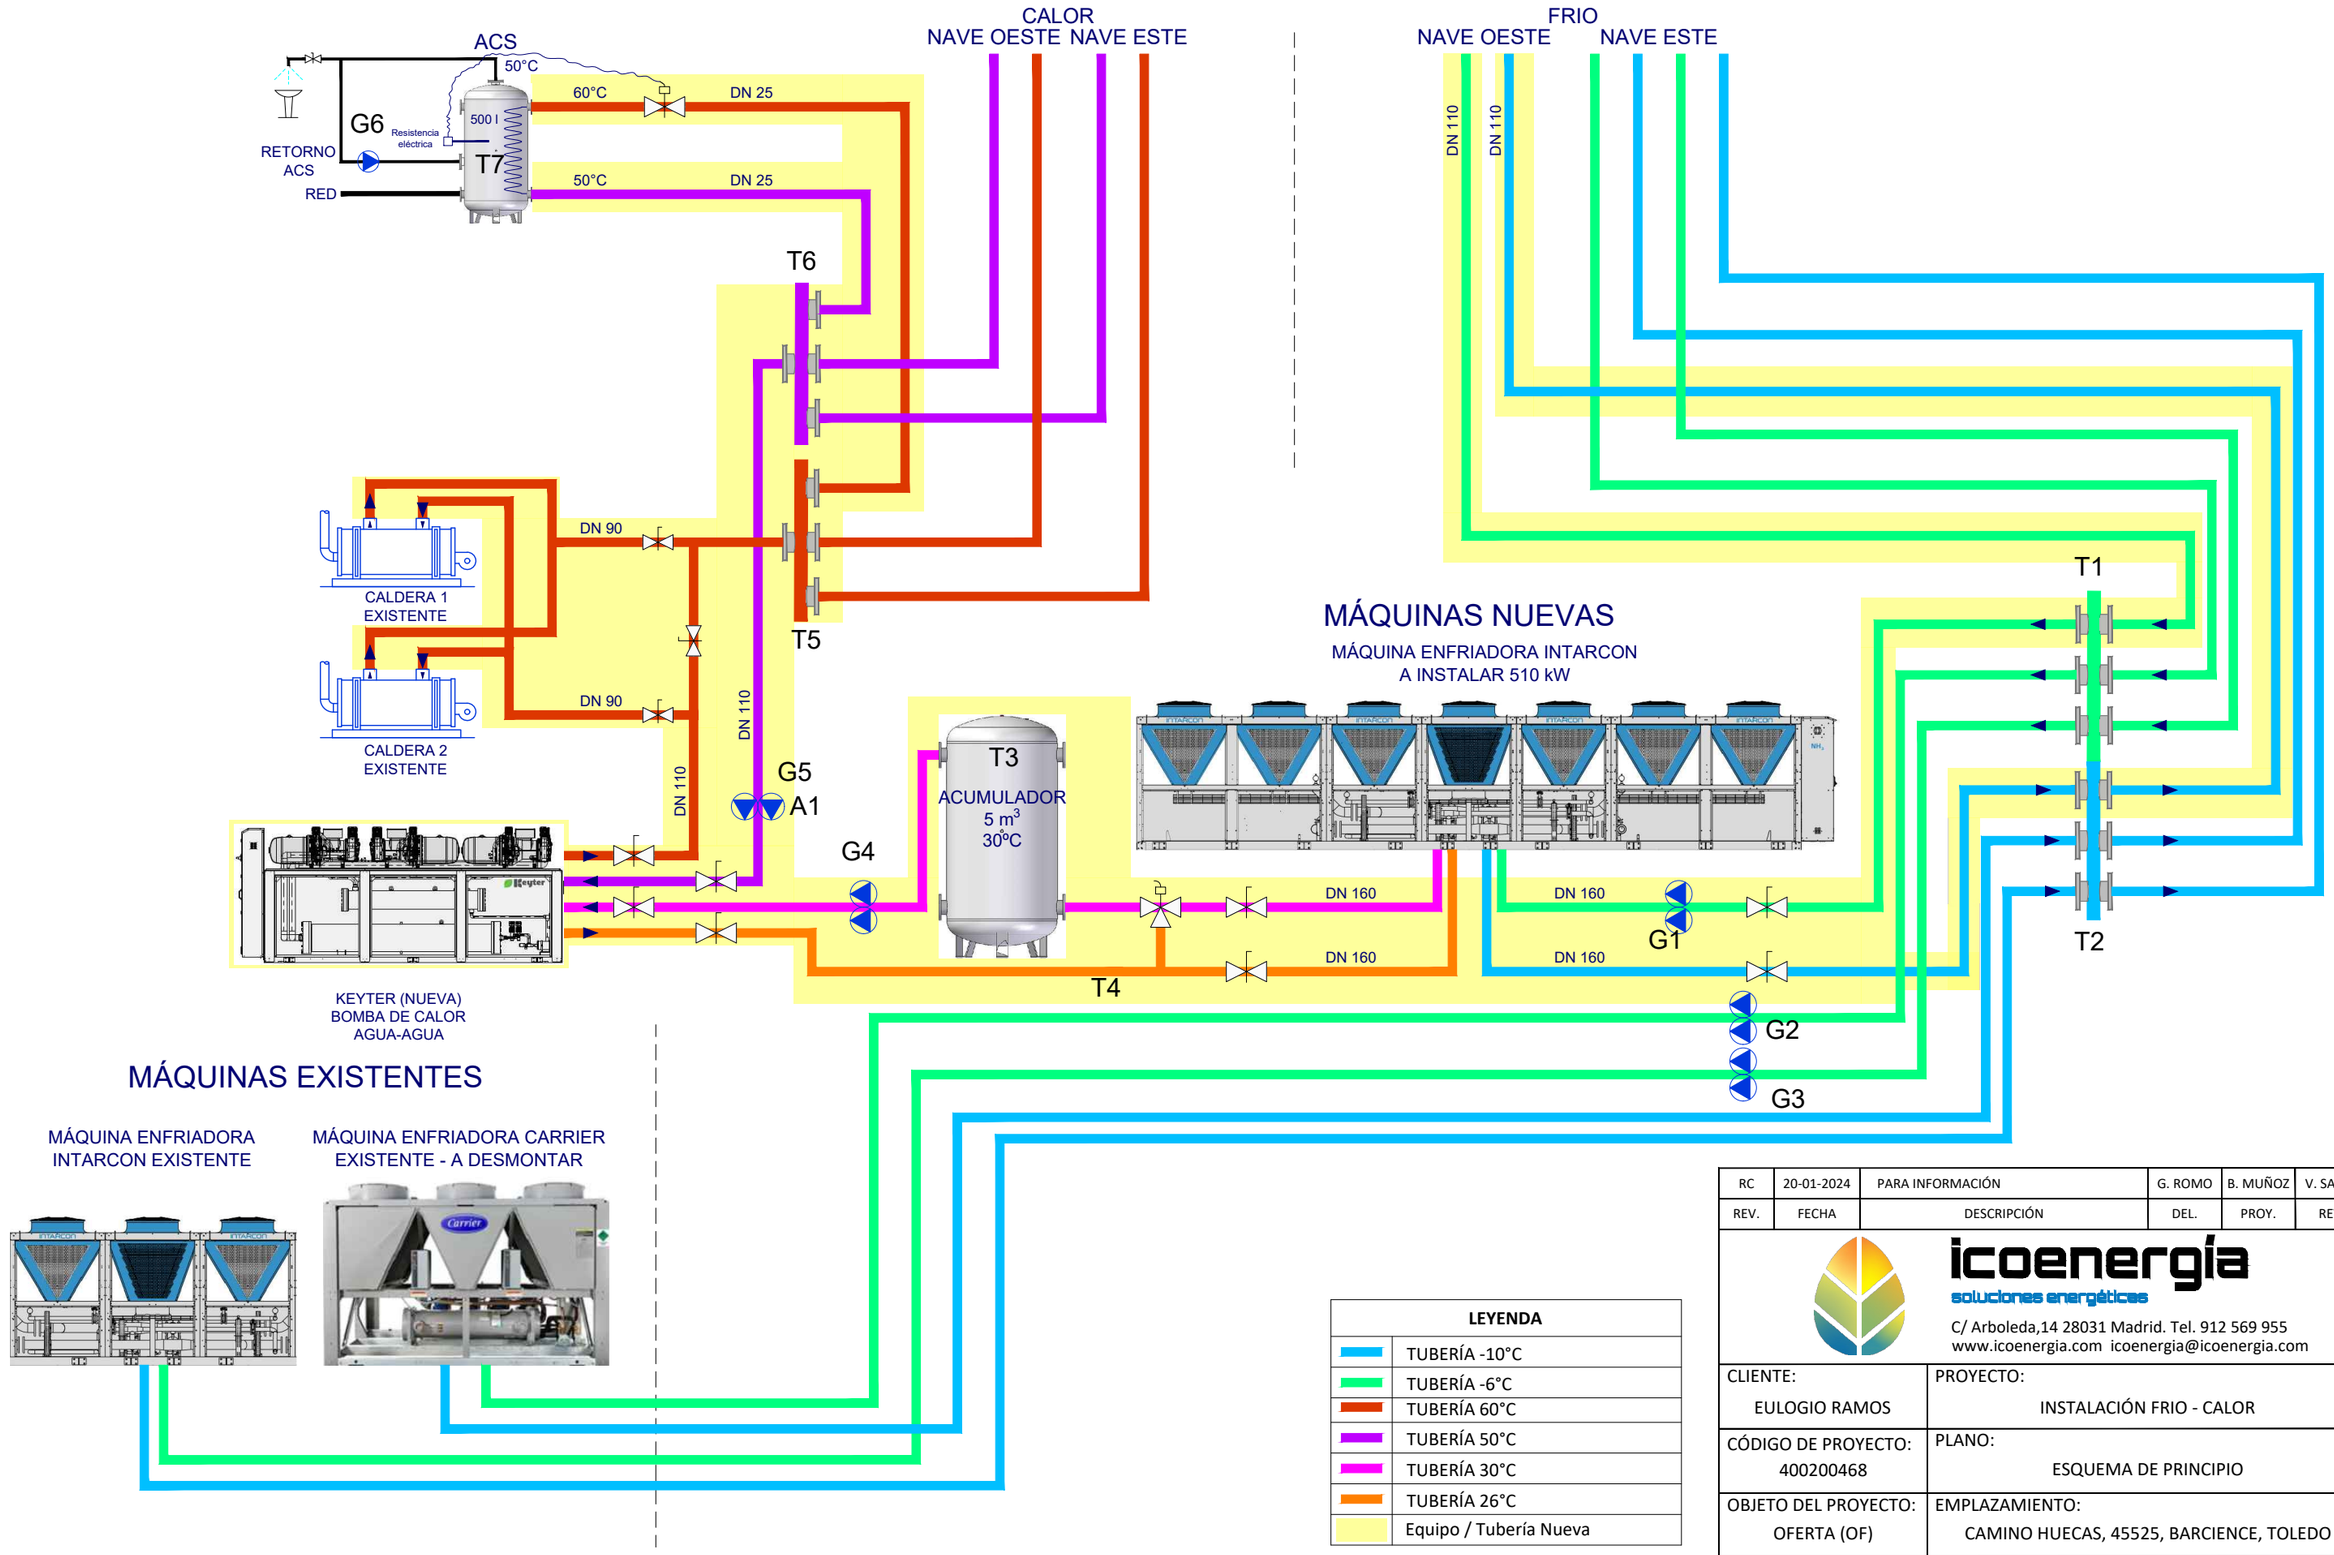

LEYENDA	
	TUBERÍA -10°C
	TUBERÍA -6°C
	TUBERÍA 60°C
	TUBERÍA 50°C
	TUBERÍA 30°C
	TUBERÍA 26°C
	Equipo / Tubería Nueva

REV.	FECHA	DESCRIPCIÓN	DEL.	PROY.	REV.
RC	20-01-2024	PARA INFORMACIÓN	G. ROMO	B. MUÑOZ	V. SAENZ

icoenergía
soluciones energéticas
C/ Arboleda,14 28031 Madrid. Tel. 912 569 955
www.icoenergia.com icoenergia@icoenergia.com

CLIENTE: EULOGIO RAMOS	PROYECTO: INSTALACIÓN FRIO - CALOR	
CÓDIGO DE PROYECTO: 400200468	PLANO: ESQUEMA DE PRINCIPIO	
OBJETO DEL PROYECTO: OFERTA (OF)	EMPLAZAMIENTO: CAMINO HUECAS, 45525, BARCIENCE, TOLEDO	
CÓDIGO DEL PLANO: P-PROC-ESQ.PRINCIPIO-0	ESCALA: SE (A3)	HOJA: 01 de 02

400200468-P-PROC-ESQ.PPIO-RC.dwg
Este plano es propiedad de ICOENERGÍA. Queda prohibida la reproducción, total o parcial del mismo y el uso de su contenido, sin el previo y expreso consentimiento escrito por parte de ICOENERGÍA s.a